


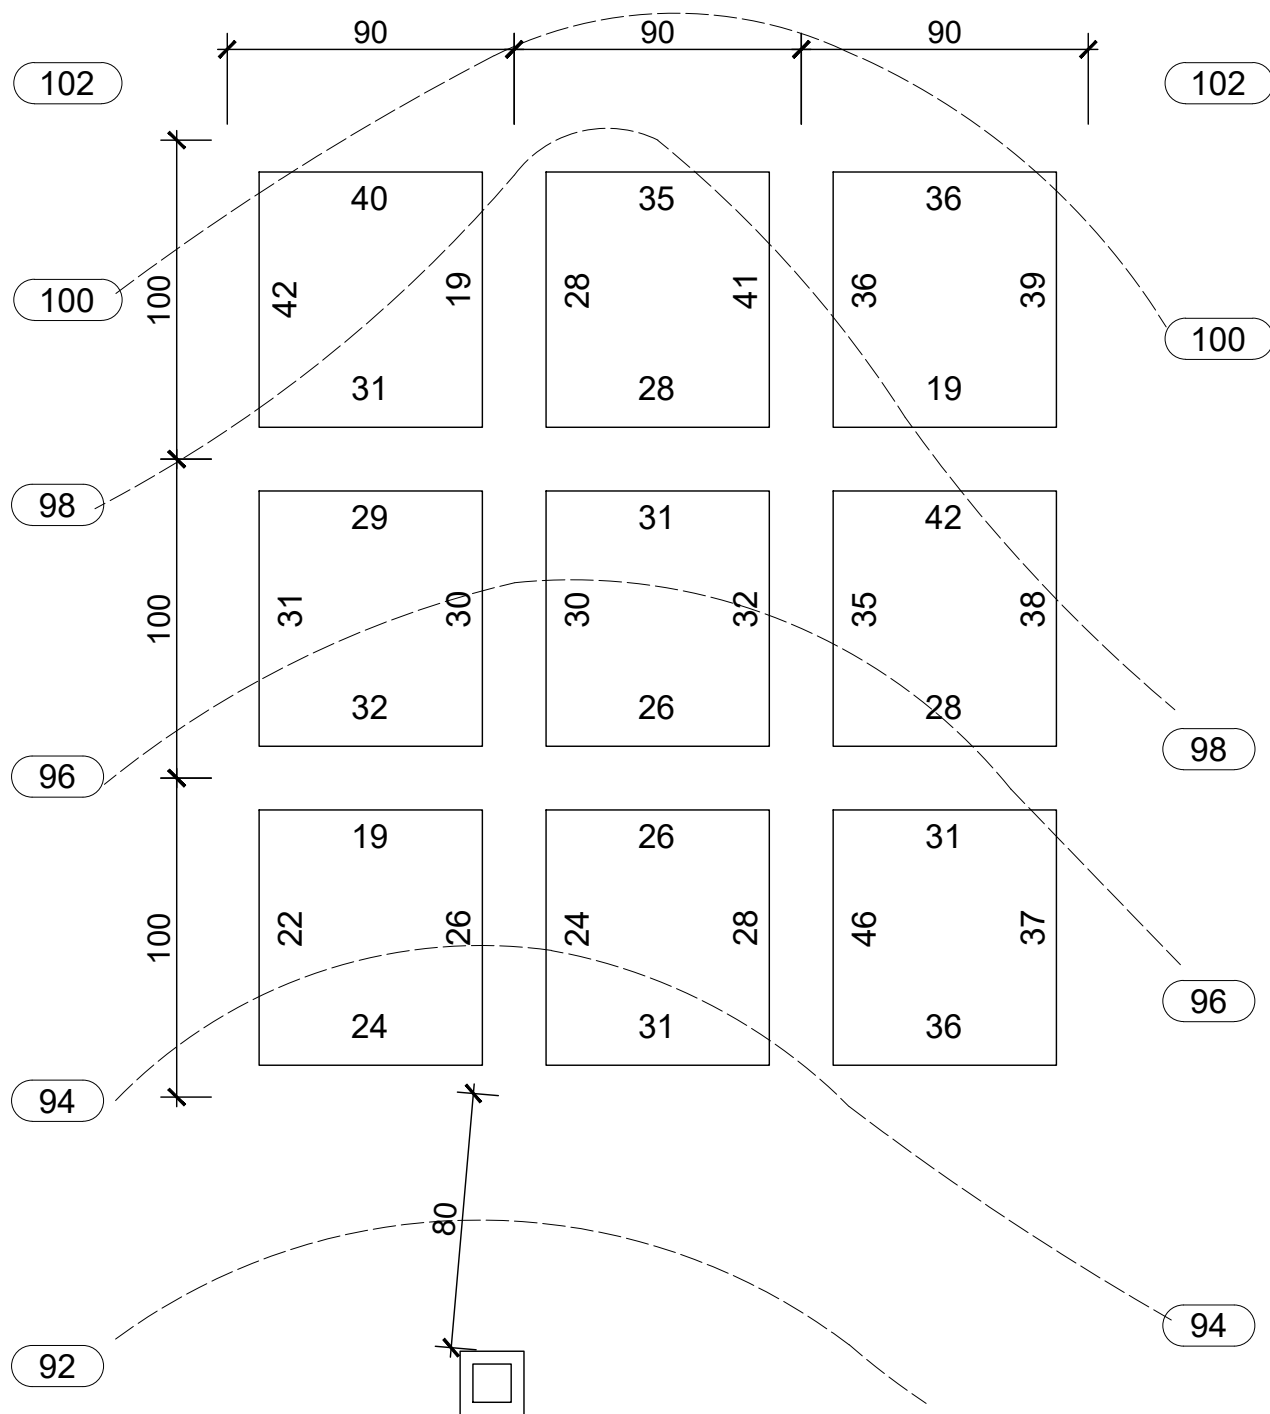

PLANTA INICIAL

HABITANTES, CURVAS DE NIVEL Y PLANTA DE TRATAMIENTO


SIMBOLOGÍA

(96)	Curva de nivel
□ PTAR	Planta de tratamiento de aguas R.

CRITERIOS DE DISEÑO

Periodo de diseño:	32 años
Factor de tasa de crecimiento:	2.78 %
Dotación:	200 L/h/d
Factor de retorno:	75%
Densidad de vivienda:	6 h/v
Ancho de calle:	10 m

EL NUMERO DENTRO DE LAS MANZANAS
INDICA EL NUMERO DE VIVIENDAS ACTUALES

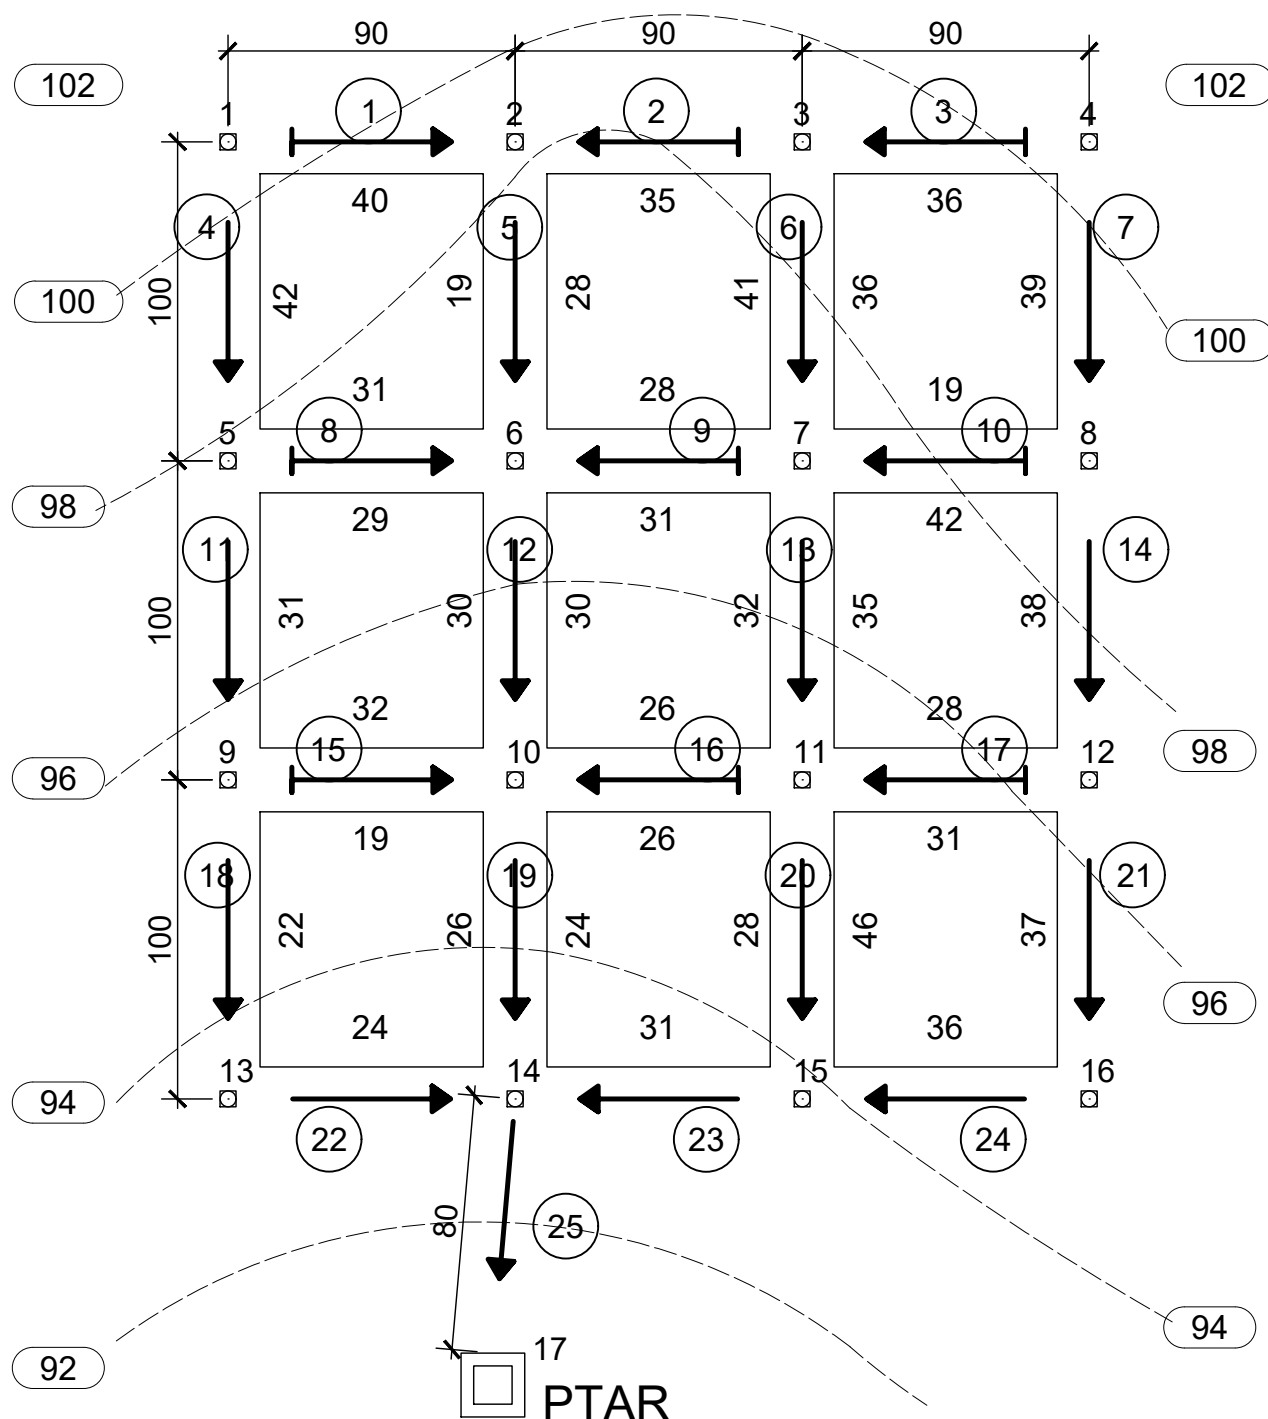

PLANTA DISEÑO

POZOS, PUNTOS DE DESFOGUE, TUBERÍAS INICIO - SEGUIMIENTO

SIMBOLOGÍA	
□ 1	Pozo número
⑪	Punto de desfogue número
⑨⑥	Curva de nivel
└─▶	Tubería de inicio
─▶	Tubería de seguimiento
□ PTAR	Planta de tratamiento de aguas R.

CRITERIOS DE DISEÑO	
Periodo de diseño:	32 años
Factor de tasa de crecimiento:	2.78 %
Dotación:	200 L/h/d
Factor de retorno:	75%
Densidad de vivienda:	6 h/v
Ancho de calle:	10 m

EL NUMERO DENTRO DE LAS MANZANAS
INDICA EL NUMERO DE VIVIENDAS ACTUALES